

"TASDIQLAYMAN"
ishlab chiqarish menejeri
"CCI Samarqand Limited"MCHJ
_____Muhammad Ashfaq

CCI SAMARQAND LIMITED ZAVODI ISHCHI-XODIMLARINI EVAKUVATSIYA QILISH REJASI

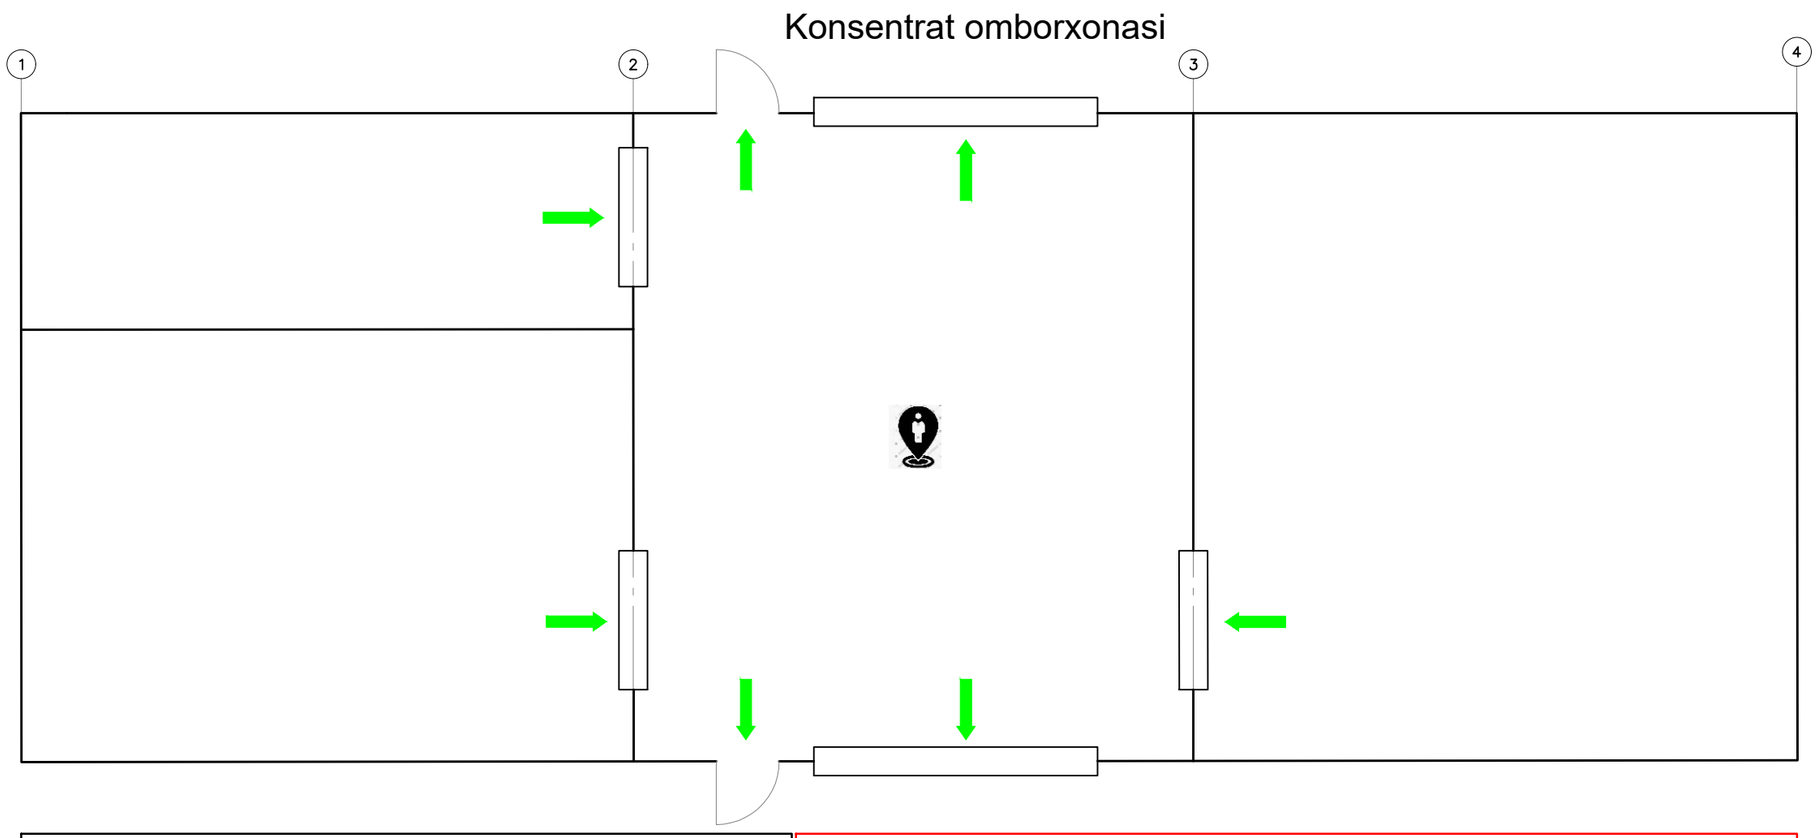

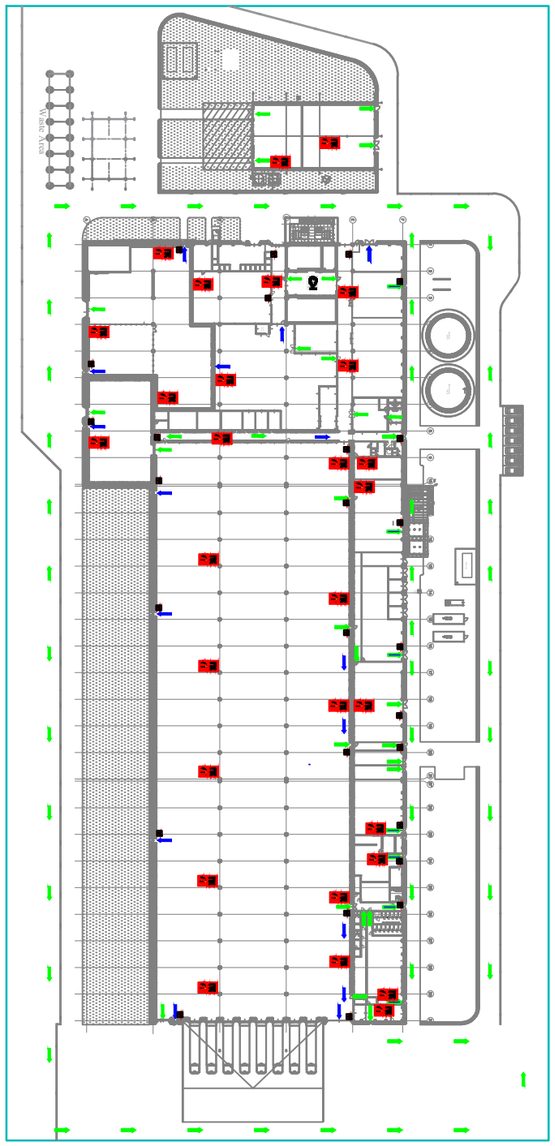

Условные обозначения /SHartli belgilar

- Основные пути эвакуации / Evakuvasiyaning asosiy yo'llari
- Запасные пути эвакуации / Zaxira evakuvasiya yo'llari
- Огнетушитель / Yongin o'chirgich
- Ручной пож. извещатель / Qo'lda yong'in dedetori
- Пожарный кран / Yong'in krani
- Вы здесь / Siz shu yerdasiz.

Favqulotdda vaziyatda !

1.Xavsizlik xizmati FBV (101)ga xabar bering yoki qo'lda yong'in detektoridan foydalaning.

2.Yig'ish punkitiga (ofis binosi oldida) evakuvasiya yo'llaridan keyin binolarni tark eting . jabirlanganlarga yordam bering.

3.Iloji bo'lsa birlamchi yong'inga qarshi vositalaridan foydalangan holda yong'inni o'chirish choralarini ko'ring

В СЛУЧАЕ ЧРЕЗВЫЧАЙНОЙ СИТУАЦИИ!

1.Сообщить МЧС (101) или задействовать ручной пожарный извещатель

2.Покинуть помещение, следуя эвакуационным путям на пункт сбора (перед зданием завода), оказать помощь пострадавшим.

3.По возможности, принять меры к тушению,используя первичные средства пожаротушения