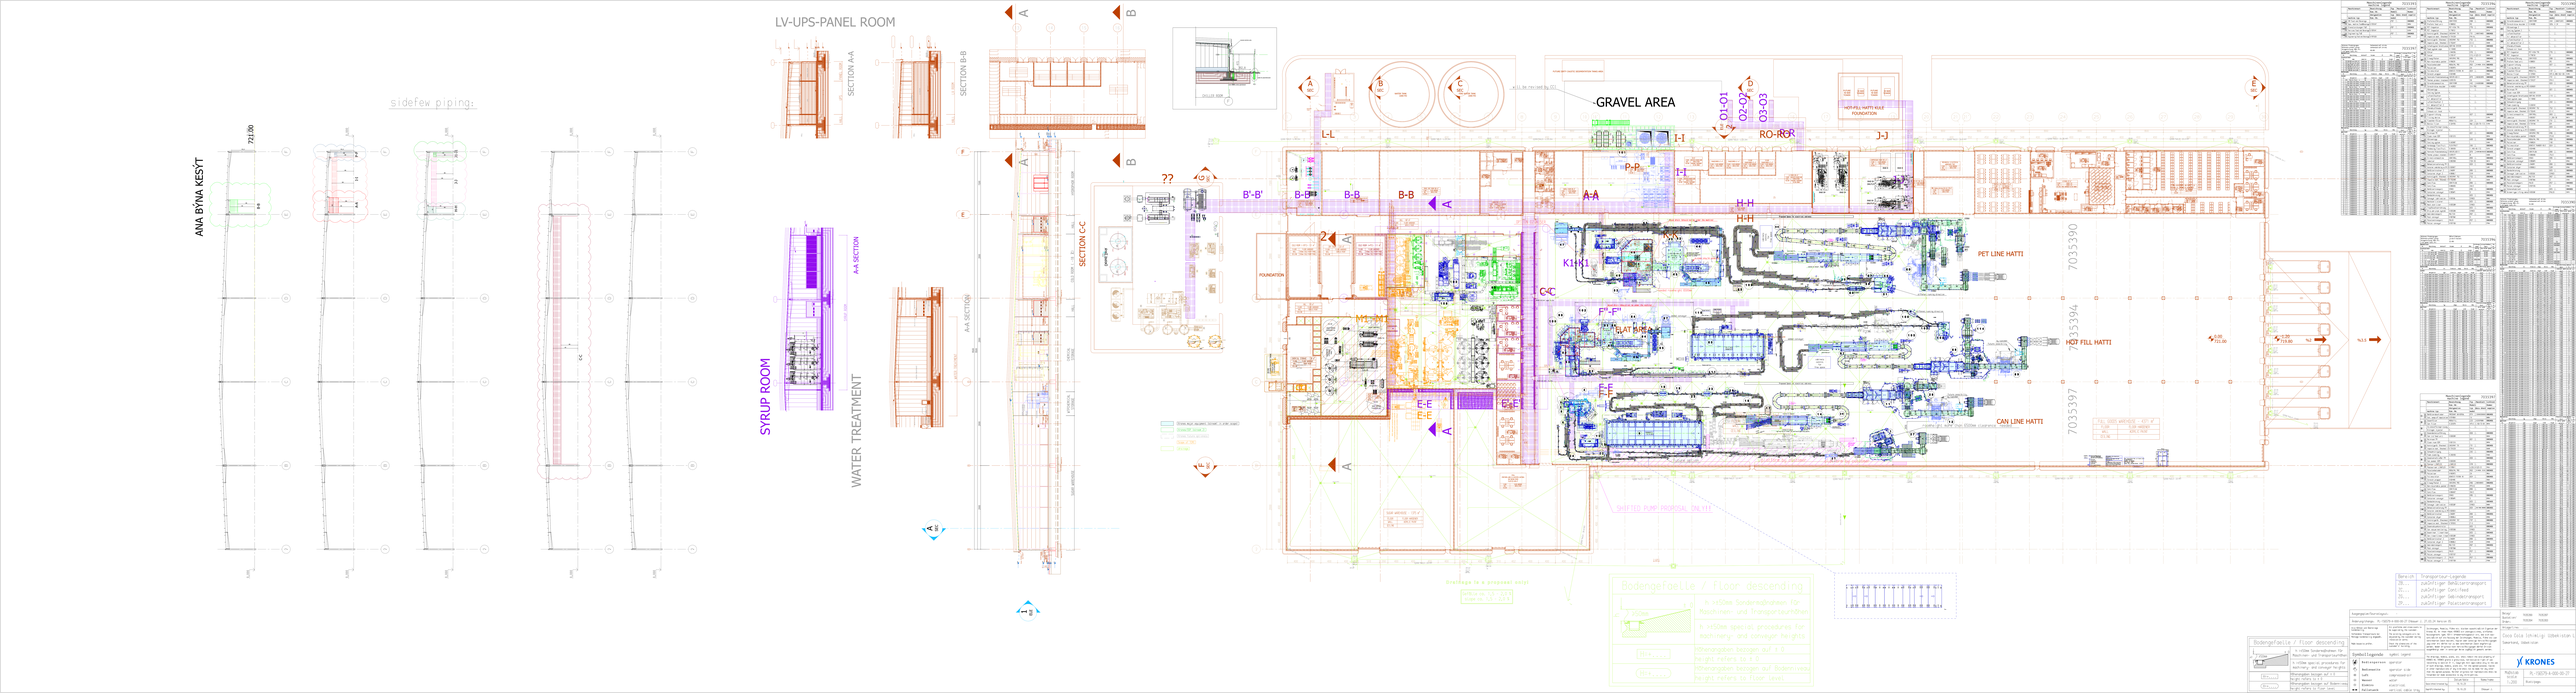

LV-UPS-PANEL ROOM
GRAVEL AREA
SYRUP ROOM
WATER TREATMENT
SECTION A-A
SECTION B-B
SECTION C-C
A-A SECTION
sidefew piping:
ANA BİNA KESİT
PET LINE HATTI
HOT FILL HATTI
CAN LINE HATTI
FLAT LINE
SHIFTED PUMP PROPOSAL ONLY!!
Bodengefälle / Floor descending
KRONES